

SYMBOLS LEGEND

| SYMBOL/MARKER | DESCRIPTION   |
|---------------|---|
|               | DETAIL REFERENCE - SEE DETAIL NUMBER (DET) ON INDICATED SHEET (SHT)                                                                                  |
|               | DETAIL REFERENCE WITH LINE TO INDICATE AREA OF CUT FOR VIEW - SEE DETAIL NUMBER (DET) ON INDICATED SHEET (SHT)                                       |
|               | DETAIL REFERENCE WITH LINE TO INDICATE AREA OF CUT FOR VIEW AND FLAG TO INDICATE DIRECTION OF VIEW- SEE DETAIL NUMBER (DET) ON INDICATED SHEET (SHT) |
|               | ENLARGED DETAIL REFERENCE CALLOUT - SEE DETAIL NUMBER (DET) ON INDICATED SHEET (SHT)                                                                 |
|               |   |
|               | INTERIOR ELEVATION REFERENCE - SEE DETAIL NUMBER (DET) ON INDICATED SHEET (SHT) AND CORRESPONDING DIRECTIONAL INDICATOR A, B, C & D AS OCCURS        |
|               | WINDOW IDENTIFICATION SYMBOL (NUMBER OR LETTER)- SEE WINDOW SCHEDULE                                                                                 |
|               | DOOR IDENTIFICATION SYMBOL (NUMBER OR LETTER)- SEE DOOR SCHEDULE                                                                                     |
|               | VARIOUS KEYNOTES - SEE SCHEDULES OR NOTES AS INDICATED BY MARKER TYPE                                                                                |
|               |   |
|               |   |
|               |   |
|               | SECTION CUT MARKER - SEE SECTION LETTER (SEC) ON REFERENCED SHEET (SHT)                                                                              |
|               | GRAPHICAL SCALE AS SHOWN ON PLANS AND DETAILS   |
|               | CONTINUOUS DIMENSIONAL LUMBER (RAFTERS, JOISTS, LEDGERS, BEAMS) WITH SIZE AS INDICATED BY DRAWINGS                                                   |
|               | DIMENSIONAL LUMBER BLOCKING BETWEEN CONTINUOUS LUMBER FRAMING (RAFTERS, JOISTS, LEDGERS, BEAMS, ETC.) WITH SIZE AS INDICATED BY DRAWINGS             |
|               | FINISHED CARPENTRY ELEMENTS (CASEWORK, MOLDINGS, ETC.) SHOWN WITH WOODGRAIN HATCHING                                                                 |
|               | GYPSUM BOARD MATERIAL - TYPE AND THICKNESS PER DRAWINGS                                                                                              |
|               | PLYWOOD MATERIAL - TYPE AND THICKNESS PER DRAWINGS                                                                                                   |
|               | PLAN VIEW NORTH ARROW L- PROJECT NORTH INDICATED BY "NORTH" AND TRUE NORTH INDICATED BY ARROW                                                        |
|               | NATURAL OR ORIGINAL EARTH IN CUT DETAIL VIEW   |
|               | COMPACTED EARTH IN CUT DETAIL VIEW   |
|               | BACKFILL EARTH IN CUT DETAIL VIEW   |
|               | GLASS IN ELEVATION VIEW   |

LEGEND NOTES:  
SEE ADDITIONAL SHEETS FOR MORE LEGENDS AND SYMBOLS AS MAY OCCUR PER SPECIFIC SHEETS, OR MAY DIFFER BY CONSULTANT LEGENDS ON CONSULTANT-PROVIDED SHEETS OR DRAWINGS.

GENERAL INFORMATION

CODE COMPLIANCE

BUILDING DESIGN AND CONSTRUCTION UTILIZES THE FOLLOWING CODES:

- 2022 California Residential Code (CRC)
- 2022 California Building Code (CBC)
- 2022 California Mechanical Code (CMC)
- 2022 California Electrical Code (CEC)
- 2022 California Plumbing Code (CPC)
- 2022 California Energy Code
- 2022 California Green Building Standards Code (CalGreen)

GENERAL

- All work to be in conformance with the codes as listed above and as adopted by the local governing agency, and any applicable local ordinances.
- All conditions and dimensions shown on the plans to be verified by the Contractor, any discrepancies that require clarification or revisions to be brought to the attention of the Building Designer/Architect/Engineer before commencing with the work.
- Contractor to provide the requirements of all structural detail callouts denoted as "TYPICAL" or "TYP" at specifically noted conditions and at all like conditions throughout the project, unless otherwise noted. All details on detail sheets titled as "TYPICAL", and not directly referenced on plans, to be incorporated at occurring locations throughout the project. Requirements of details not denoted or titled as "TYPICAL" to be provided at the specific location shown on the plan and adjacent areas as applicable. Requirements of details denoted as "SIMILAR" or "SIM" to be provided with differences as indicated or implied on referenced details and plans.
- Details may be depicted diagrammatically. For example, roof pitches, floor/roof/wall thicknesses, framing members, etc., may differ in scale from actual proposed conditions. Details to be understood in context with other drawings conveying architectural design intent.
- Structural design or review of temporary shoring, additional reinforcing, bracing, formwork, scaffolding, trenchwork, erection methods, etc. required for proper construction of the project to be the responsibility of the Contractor.
- Shop drawings are an aid for field placement and are superseded by the architectural drawings. It to be the responsibility of the General Contractor to make certain that all construction is in full agreement with the latest approved contract documents.
- Dimensions, unless otherwise shown, are to centerline of columns and beams, or to the face of concrete surfaces and rough framing.
- The contract drawings and specifications represent the finished structure, and, except where specifically shown, do not indicate the method or means of construction. The Contractor to supervise and direct the work and to be solely responsible for all construction means, coordination of trades, construction methods, procedures, techniques, safety, and construction sequence.

PRODUCT SUBSTITUTIONS

- Material substitutions to be submitted to the Building Designer/Architect/Engineer for review prior to use. Substitution reviews may require additional design costs. These additional costs to be paid by the person or company requesting the substitution.
- Substituted products to have ICC-ES approval and to be installed per product manufacturer's specifications. Substituted product materials, finishes, details, and installation to be of a nature similar to originally specified product so as to not conflict with any intended structural or architectural design conditions, whether depicted or implied on plans or specifications. The substituted product to have design values (i.e. design loads, impact resistance, etc.) which to be equal to or greater than the originally specified product. Any and all warranties offered by the originally specified product manufacturer for the item to be substituted to have similar warranties offered by the substituted product manufacturer. Submit to the Building Designer/Architect/Engineer a list of only the items to be substituted, complete with all pertinent material including but not limited to manufacturer's supplied design loads listed for the originally specified product and the proposed substitution product.
- 

ABBREVIATIONS

WHERE POSSIBLE, ABBREVIATIONS ARE AVOIDED IN PREFERENCE FOR VERBOSE, CLEARLY DESCRIPTIVE INFORMATION. HOWEVER, ABBREVIATIONS MAY EXIST IN SOME DRAWINGS AND SHOULD BE INTERPRETED IN CONTEXT OF THEIR USE ACCORDING TO THE LIST BELOW.

SEE GENERAL INFORMATION SHEETS FROM PROJECT CONSULTANTS AS ABBREVIATIONS MAY BE DIFFERENT FROM DIFFERENT DISCIPLINES OR CONSULTANTS.

|          |                                                        |         |                                                  |
|----------|--------------------------------------------------------|---------|--------------------------------------------------|
| 1PH      | SINGLE-PHASE                                           | D       | DEPTH; DEEP; PENNY (NAIL)                        |
| 1P       | SINGLE POLE                                            | D       | ONE-WAY                                          |
| 1WAY     | ONE-WAY                                                | D CHEM  | DRY CHEMICAL                                     |
| 2/C      | TWO-CONDUCTOR                                          | D LABEL | CLASS D DOOR                                     |
| 2WAY     | TWO-WAY                                                | D&S     | DISPLAY AND STORAGE                              |
| 3/C      | THREE-CONDUCTOR                                        | D1S     | DRESSED ONE SIDE                                 |
| 3PH      | THREE-PHASE                                            | D2S     | DRESSED TWO SIDES                                |
| 3PLY     | THREE-PLY                                              | D4S     | DRESSED FOUR SIDES                               |
| A        | CLASS A DOOR                                           | DA      | DRAINAGE AREA; DISABLE                           |
| A LABEL  | AIR CONDITION                                          | DAP     | DUCT ACCESS PANEL                                |
| A/C      | AIR CONDITIONING UNIT                                  | E       | EAST; MODULUS OF ELASTICITY                      |
| A/C UNIT | ARCHITECT/ENGINEER                                     | E LABEL | CLASS E DOOR                                     |
| A/E      | AMERICAN ASSOCIATION OF COST ENGINEERS                 | EA      | EACH                                             |
| AACE     | AUTOMATIC AIR DAMPER                                   | EAR     | EXHAUST AIR REGISTER                             |
| AAD      | AMERICAN ARCHITECTURAL MANUFACTURERS ASSOCIATION       | EAT     | ENTERING AIR TEMPERATURE                         |
| AAMA     | ALARM ANNUNCIATOR PANEL                                | EC      | EDGE OF CURB                                     |
| AAP      | AUTOMATIC AIR VENT                                     | ECC     | ECCENTRIC                                        |
| AAV      | ANCHOR BOLT                                            | F       | FAHRENHEIT; FEMALE; FIRE LINE                    |
| AB       | ABANDON                                                | F BRK   | FIRE BRICK                                       |
| ABAN     | ABBREVIATION                                           | F METER | FLOWMETER                                        |
| ABBRV    | AXIAL FLOW                                             | F/F     | FACE TO FACE                                     |
| AX FL    | AZIMUTH                                                | F1S     | FINISHED ONE SIDE                                |
| AZ       | B                                                      | F2S     | FINISH TWO SIDES                                 |
| B        | B CL                                                   | F4S     | FINISH FOUR SIDES                                |
| B CL     | BROOM CLOSET                                           | FA      | FIRE ALARM; FACE AREA; FINAL ASSEMBLY; FRESH AIR |
| BN       | BULLNOSE                                               | G       | G                                                |
| BNDG     | BONDING                                                | G       | GIRDER; GROUND; NATURAL GAS                      |
| BO       | BLOWOFF                                                | G DISP  | GARBAGE DISPOSAL                                 |
| BOCA     | BUILDING OFFICIALS AND CODE ADMINISTRATORS ASSOCIATION | G LN    | GAS LINE                                         |
| BOS      | INTERNATIONAL                                          | GA      | GAGE; GYPSUM ASSOCIATION                         |
| BOT      | BOTTOM OF STEEL                                        |         |                                                  |
| BOT F    | BOTTOM                                                 |         |                                                  |
| C        | BOTTOM FACE                                            |         |                                                  |
| C        | CELSIUS; CHANNEL                                       |         |                                                  |
| CLG      | C                                                      |         |                                                  |
| COP      | CEILING                                                |         |                                                  |
| COR      | COPING; COEFFICIENT OF PERFORMANCE (HEATING)           |         |                                                  |
| CORN     | CHANGE ORDER REQUEST                                   |         |                                                  |
| CORR     | CORNICE                                                |         |                                                  |
| CORRES   | CORRIDOR; CORRECT                                      |         |                                                  |
| COTG     | CORRESPOND                                             |         |                                                  |
| COV      | CLEANOUT TO GRADE                                      |         |                                                  |
| COV PL   | COVER; CUT OFF VALVE                                   |         |                                                  |
| CP       | COVER PLATE                                            |         |                                                  |
| CPLG     | CONCRETE PIPE; CANDLEPOWER; CONTROL PANEL              |         |                                                  |
| CPM      | COUPLING                                               |         |                                                  |
| CPRS     | CRITICAL PATH METHOD                                   |         |                                                  |
| CPT      | COMPRESSIBLE                                           |         |                                                  |
| CPVC     | CARPET; CONTROL POWER TRANSFORMER                      |         |                                                  |
|          | CHLORINATED POLYVINYL CHLORIDE                         |         |                                                  |

CONTACTS & CONSULTANTS LIST

OWNER

MAILING ADDRESS: CHRIS SMITH AND PAT SMITH  
12345 OLD MAIN STREET  
ANYTOWN, CA 95555

PHONE: (707) 837-5609

EMAIL: FAKE\_EMAIL@FAKE\_EMAIL.COM

BUILDNG DESIGNER/ARCHITECT

ADDRESS: YOUR NAME GOES HERE  
YOUR (FAKE) ADDRESS GOES HERE  
YOUR (FAKE) CITY, STATE, ZIPCODE GOES HERE

STRUCTURAL ENGINEER

ADDRESS: STRUCTURAL ENGINEER FIRM NAME  
STRUCTURAL ENGINEERING FIRM ADDRESS

PHONE:

EMAIL:

CONTACT:

PROJECT NUMBER:

ELECTRICAL ENGINEER

ADDRESS:

PHONE:

CONTACT:

GEOTECHNICAL ENGINEER

ADDRESS:

PHONE:

CONTACT:

GEOTECHNICAL INVESTIGATION REPORT NUMBER:

TITLE 24 ENERGY CONSULTANT

ADDRESS:

PHONE:

CONTACT:

CAL GREEN COMPLIANCE CONSULTANT

ADDRESS:

PHONE:

CONTACT:

INTERIOR DESIGNER

ADDRESS:

PHONE:

CONTACT:

CIVIL ENGINEER

ADDRESS:

PHONE:

CONTACT:

SURVEYOR

ADDRESS:

PHONE:

CONTACT:

LANDSCAPE DESIGNER/ARCHITECT

ADDRESS:

PHONE:

CONTACT:

MECHANICAL/PLUMBING ENGINEER

ADDRESS:

PHONE:

CONTACT:

FIRE SAFETY CONSULTANT

ADDRESS:

PHONE:

CONTACT:

PROJECT INFORMATION

PROJECT DESCRIPTION:  
SINGLE FAMILY ACCESSORY DWELLING UNIT TO BE CONSTRUCTED ON AN EXISTING SINGLE FAMILY RESIDENCE PROPERTY

ASSESSOR'S PARCEL NUMBER:  
XXX-XXX-XXX

ZONING:  
R-3

TYPE OF CONSTRUCTION:  
TYPE VN

FIRE SAFETY AREA:  
STATE RESPONSIBILITY AREA or LOCAL RESPONSIBILITY AREA (CHOOSE ONE AS APPLIES)

PROJECT ADDRESS:  
1234 MAIN STREET  
ANYTOWN, CA ZIPCODE

PARCEL AREA:  
?? ACRES  
?? SQUARE FEET

PROPOSED DWELLING AREA:  
?? SQUARE FEET

GARAGE AREA:  
?? SQUARE FEET

PROPOSED ROOF AREA:  
?? SQUARE FEET

(CONSIDER ADDING THE AREAS FOR ANY OF THESE ITEMS NOT ALREADY INCLUDED ABOVE, TAKEN FROM THE SONOMA COUNTY BUILDNG PERMIT ONLINE WEBSITE: e.g. dwelling area, garage area, covered porches, decks, retained square footage retained at the face of retaining walls, storage areas, basements, etc.)



VICINITY MAP



SHEET INDEX

| Sheet List Table |                                   |
|------------------|-----------------------------------|
| Sheet Number     | Sheet Title                       |
| G-000            | COVER SHEET                       |
| A-101            | SITE PLAN                         |
| A-102            | FLOOR PLAN                        |
| A-301            | BUILDING SECTIONS                 |
| A-201            | EXTERIOR ELEVATIONS               |
| AE-103           | ELECTRICAL AND LIGHTING PLAN      |
| AS-104           | ROOF FRAMING PLAN                 |
| AS-101           | FLOOR FRAMING AND FOUNDATION PLAN |

STUDIO DESIGN

SMITH ADU  
1234 MAIN STREET  
ANYTOWN, CA  
100-100-100


| DATE                | DESCRIPTION       |
|---------------------|-------------------|
| ISSUE INFORMATION   |                   |
| DRAWING INFORMATION |                   |
| PROJECT NUMBER:     | 2602              |
| SHEET SET:          |                   |
| FILENAME:           | G-000             |
| SAVED DATE:         | 5/21/2026 2:38 PM |
| PLOT DATE:          | 5/21/2026 2:56 PM |
| LOGINNAME:          | S00740304         |
| DRAWN BY:           |                   |
| CHECKED BY:         |                   |

SHEET TITLE

COVER SHEET

G-000

SHEET OF SHEETS

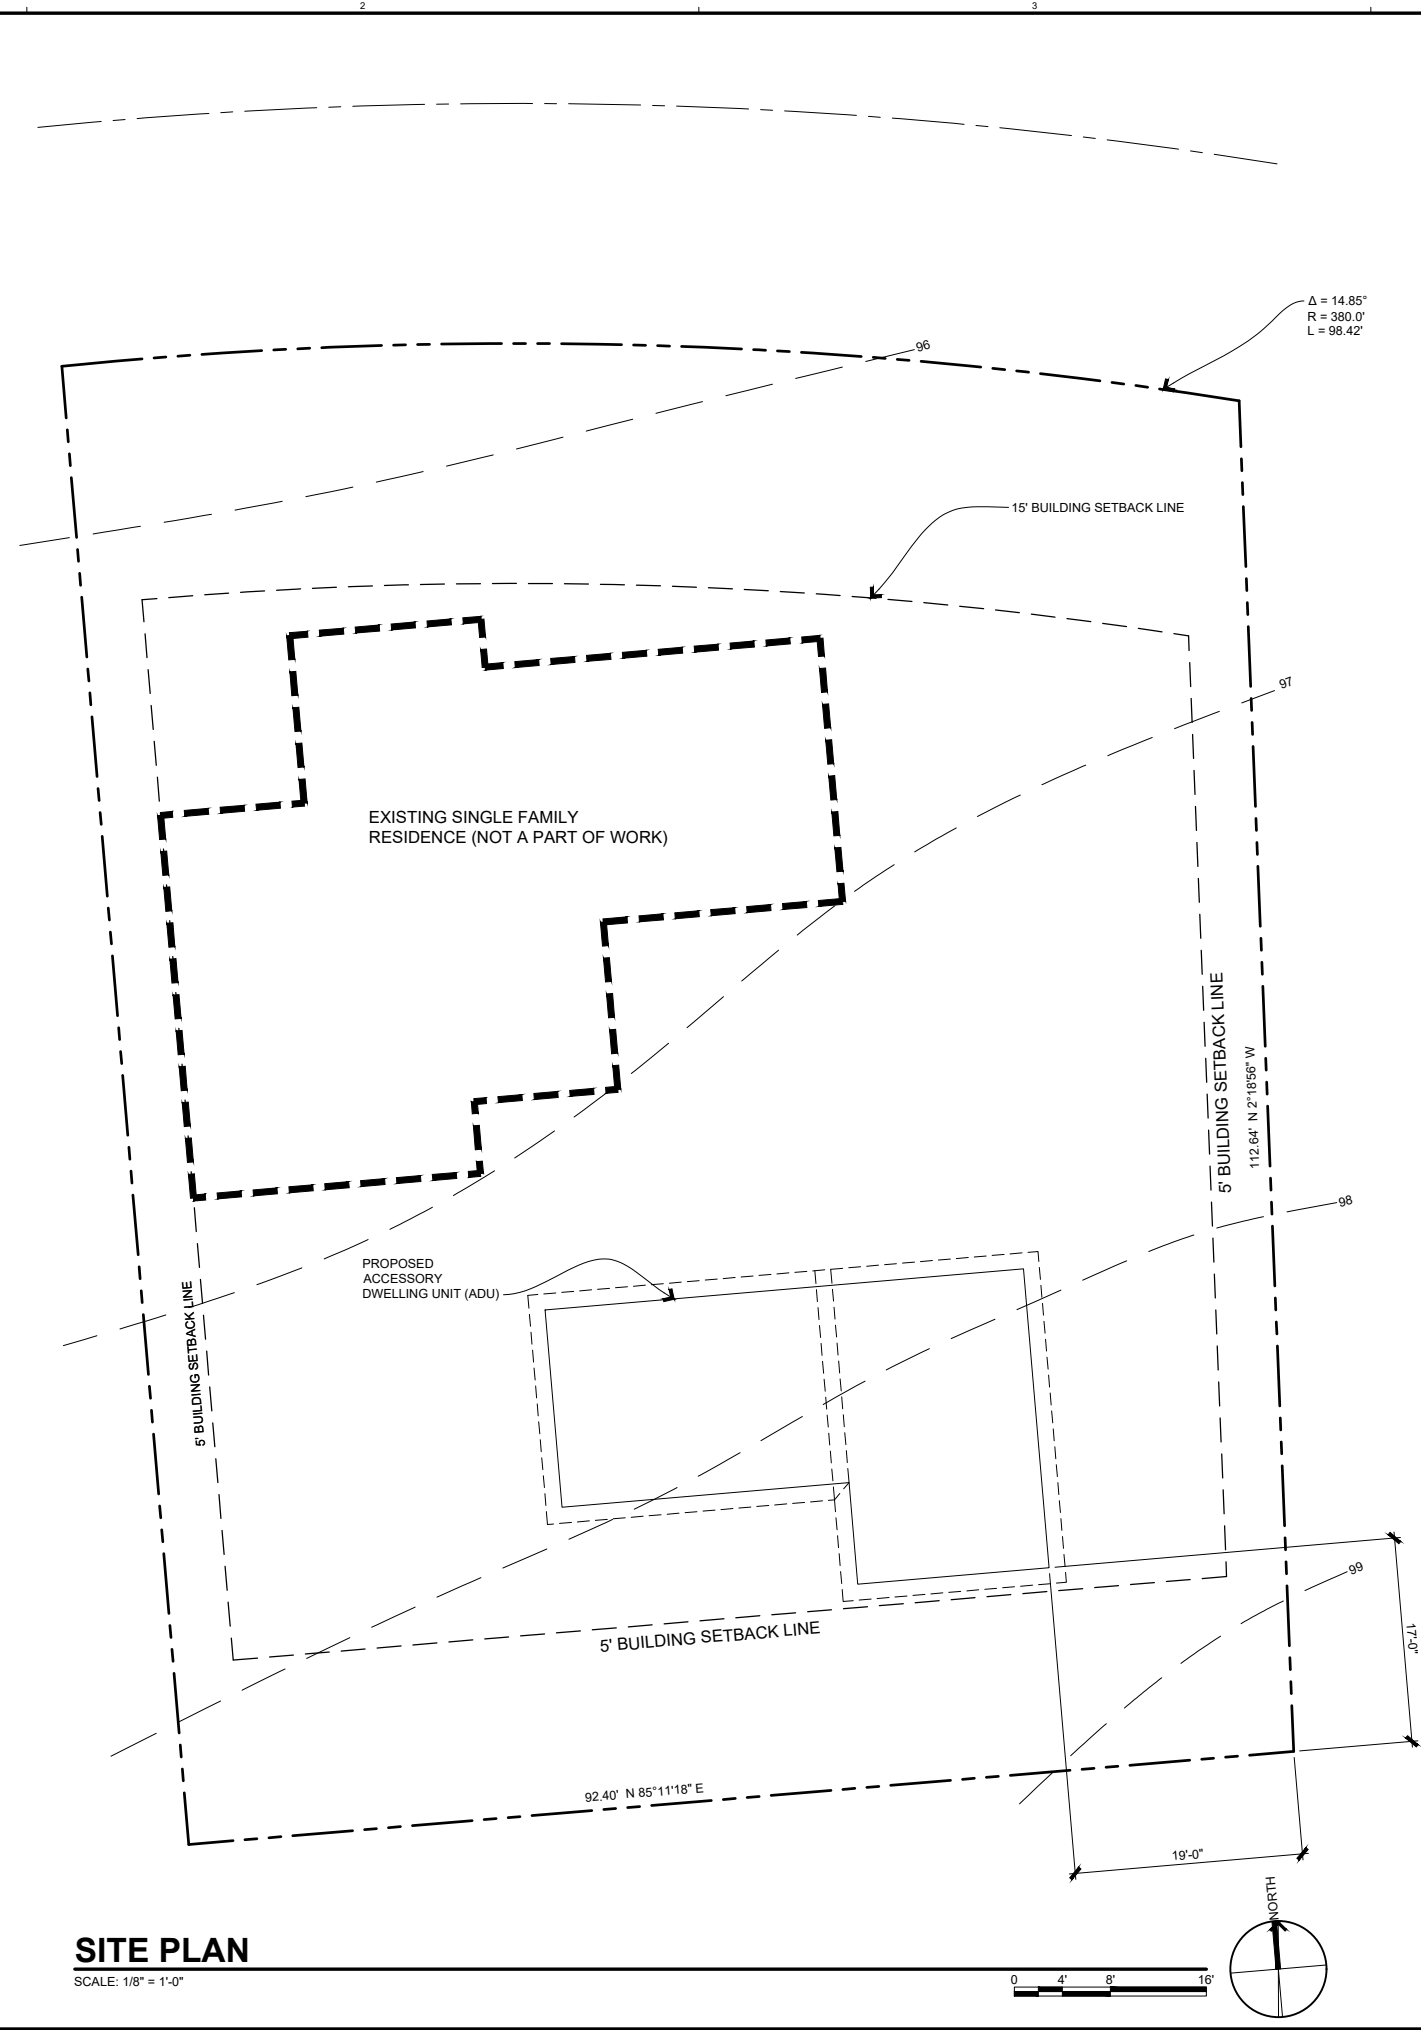

The first step in the process of identifying a problem is to recognize that there is a problem. This can be done by looking at the current situation and comparing it to what you want to achieve. Once you have identified the problem, the next step is to define the problem more clearly. This involves asking questions such as "What exactly is the problem?" and "Why is it a problem?"

## PROJECT INFORMATION

[illegible]


| ISSUE INFORMATION   |                   |
|---------------------|-------------------|
| DRAWING INFORMATION |                   |
| PROJECT NUMBER:     | 2602              |
| SHEET SET:          |                   |
| FILENAME:           | A-101             |
| SAVED DATE:         | 5/21/2026 1:48 PM |
| PLOT DATE:          | 5/21/2026 2:55 PM |
| LOGINNAME:          | S00740304         |
| DRAWN BY:           |                   |
| CHECKED BY:         |                   |

## SITE PLAN

# A-101

SHEET OF SHEETS

V:\Nayara Ayres Vieira\A-102.dwg

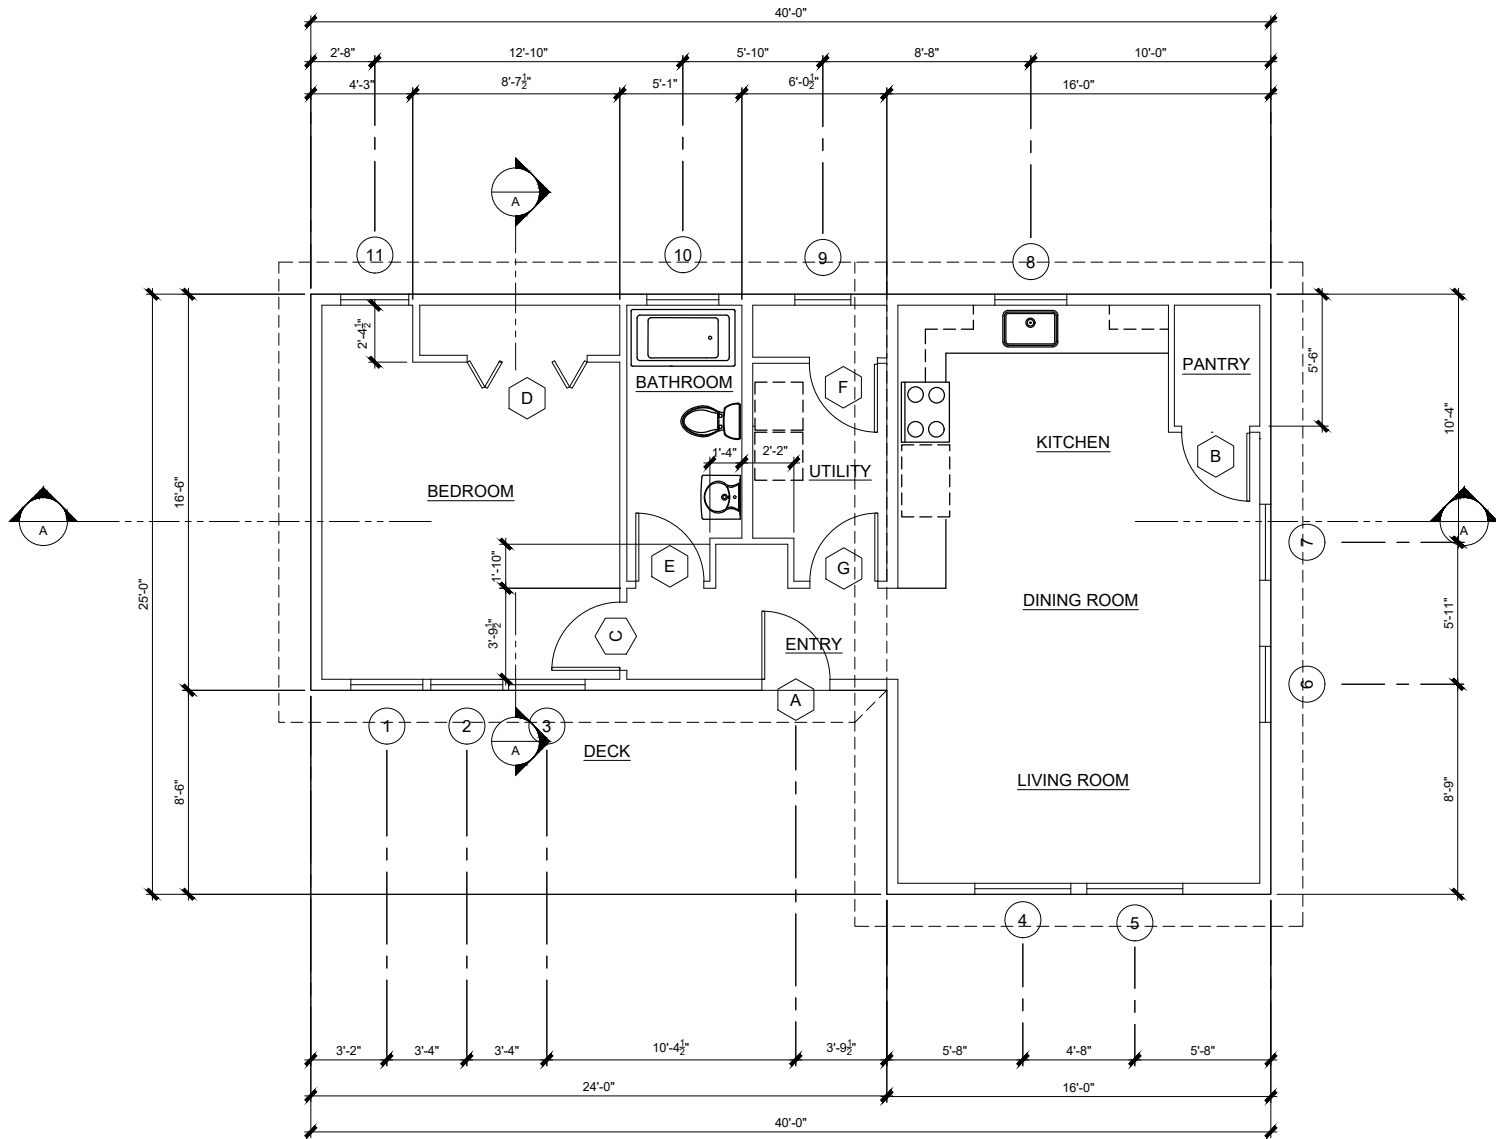

## FLOOR PLAN

SCALE: 1/4" = 1'-0"

## STUDIO DESIGN

### SEALS

### PROJECT INFORMATION

**SMITH ADU**  
**1234 MAIN STREET**  
**ANYTOWN, CA**  
**100-100-100**

| DATE                | DESCRIPTION       |
|---------------------|-------------------|
| ISSUE INFORMATION   |                   |
| DRAWING INFORMATION |                   |
| PROJECT NUMBER:     | 2602              |
| SHEET SET:          |                   |
| FILENAME:           | A-102             |
| SAVED DATE:         | 5/21/2026 1:48 PM |
| PLOT DATE:          | 5/21/2026 2:55 PM |
| LOGINNAME:          | S00740304         |
| DRAWN BY:           |                   |
| CHECKED BY:         |                   |

### SHEET TITLE


## FLOOR PLAN

# A-102

SHEET OF SHEETS




SHEET OF SHEETS

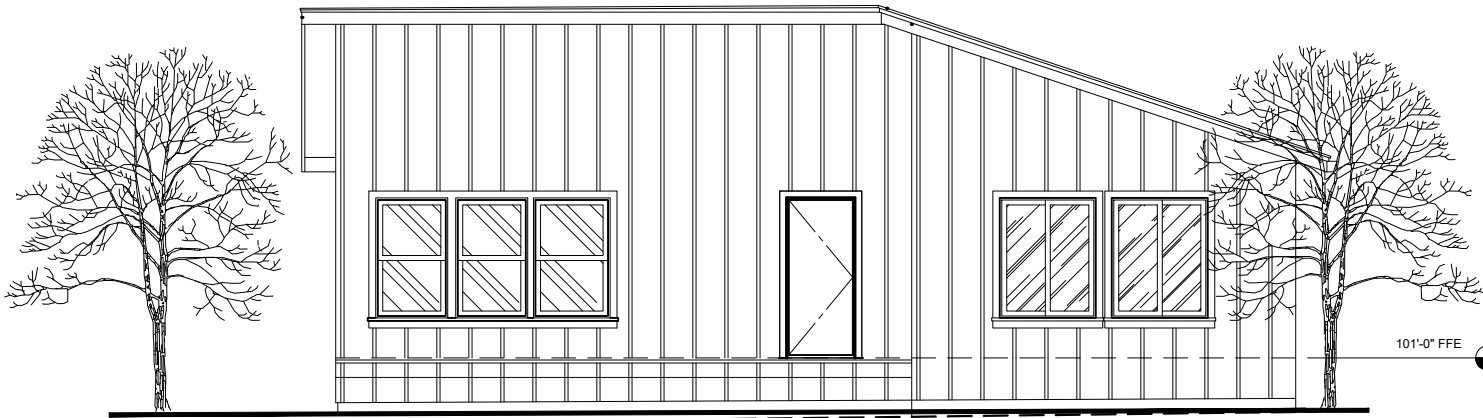

SOUTH ELEVATION

SCALE: 1/4" = 1'-0"


0 2' 4' 8'

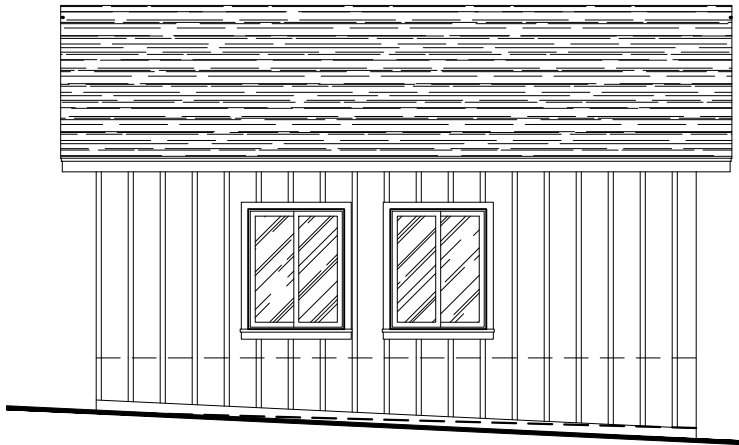

EAST ELEVATION

SCALE: 1/4" = 1'-0"


0 2' 4' 8'

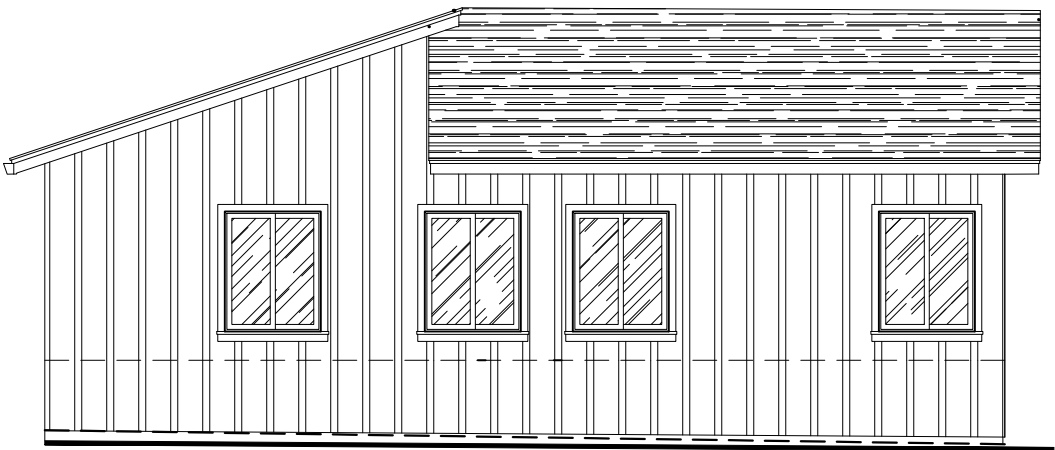

NORTH ELEVATION

SCALE: 1/4" = 1'-0"

0 2' 4' 8'

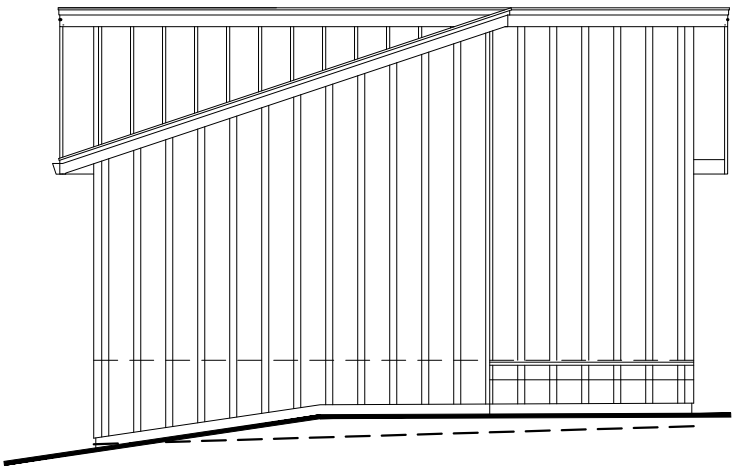

WEST ELEVATION

SCALE: 1/4" = 1'-0"

0 2' 4' 8'

STUDIO DESIGN

SEALS

PROJECT INFORMATION

SMITH ADU  
1234 MAIN STREET  
ANYTOWN, CA  
100-100-100

DATE DESCRIPTION

ISSUE INFORMATION

DRAWING INFORMATION


PROJECT NUMBER: 2602  
SHEET SET:  
FILENAME: A-201  
SAVED DATE: 5/21/2026 2:51 PM  
PLOT DATE: 5/21/2026 2:56 PM  
LOGINNAME: S00740304  
DRAWN BY:  
CHECKED BY:

SHEET TITLE

EXTERIOR  
ELEVATIONS

A-201

SHEET OF SHEETS

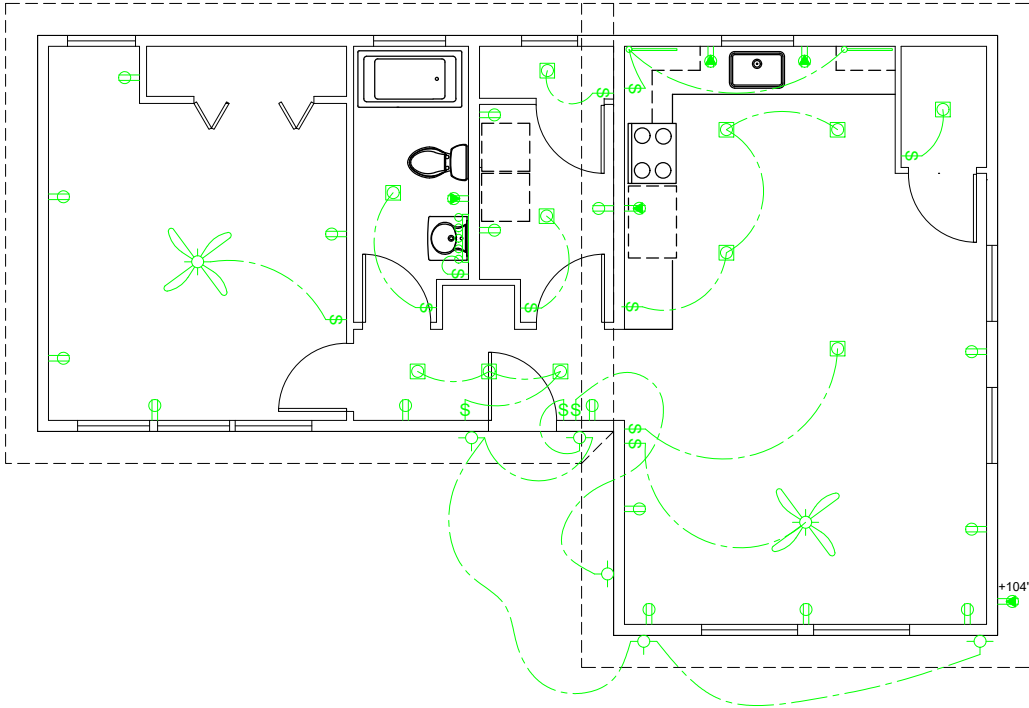

## ELECTRICAL / LIGHTING PLAN

SCALE: 1/4" = 1'-0"



### ELECTRICAL SYMBOL LEGEND

| SYMBOL | DESCRIPTION                              |
|--------|------------------------------------------|
|        | SMOKE DETECTOR                           |
|        | SINGLE POLE SWITCH                       |
|        | THREE-WAY SWITCH                         |
|        | DIMMER SWITCH                            |
|        | 110V DUPLEX RECEPTACLE                   |
|        | 220 VOLT RECEPTACLE                      |
|        | WATERPROOF GFCI DUPLEX RECEPTACLE        |
|        | HALF-HOT DUPLEX RECEPTACLE               |
|        | GROUND FAULT INTERRUPT DUPLEX RECEPTACLE |
|        | QUADPLEX RECEPTACLE                      |
|        | FLOOR/CEILING MOUNTED DUPLEX RECEPTACLE  |
|        | DOOR BELL                                |
|        | RECESSED LED                             |
|        | RECESSED LED WALL WASHER                 |
|        | RECESSED COMPACT FLUORESCENT             |
|        | TELEVISION CABLE                         |
|        | ADJUSTABLE TRACK FIXTURE                 |
|        | EXHAUST FAN                              |
|        | MULTI-LAMP VANITY                        |
|        | UNDERCOUNTER LED TAPE LIGHT              |
|        | 24" FLUORESCENT                          |
|        | FANLIGHT COMBO UNIT                      |
|        | WALL MOUNTED LED FIXTURE                 |
|        | CEILING MOUNTED LED FIXTURE              |
|        | CEILING PADDLE FAN                       |

### ELECTRICAL/LIGHTING PLAN NOTES

1. MAINTAIN A CLEARANCE OF 36" IN FRONT OF ELECTRICAL DISTRIBUTION AND SUB PANELS. (CEC 110.26)
2. PROVIDE A MINIMUM OF ONE 20 AMP RECEPTACLE IN AREAS DESIGNATED FOR LAUNDRY EQUIPMENT. (CEC 110.26)
3. KITCHENS AND DINING AREAS MUST HAVE A MINIMUM OF TWO 20 AMP CIRCUITS. KITCHEN COUNTER OUTLETS MUST BE INSTALLED IN EVERY COUNTER SPACE 12" OR WIDER, NOT GREATER THAN 4' O.C. AND WITHIN 24" OF THE END OF ANY COUNTER SPACE. (CEC 210.52f)
4. GFCI OUTLETS ARE REQUIRED FOR ALL KITCHEN RECEPTACLES THAT ARE DESIGNED TO SERVE COUNTERTOP SURFACES, IN BATHROOMS, IN UNDERFLOOR SPACES AT OR BELOW GRADE LEVEL, IN EXTERIOR OUTLETS, IN LAUNDRY AREAS, AND IN ALL GARAGE OUTLETS NOT DEDICATED TO A SINGLE DEVICE OR APPLIANCE. (CEC 210.8) ALL DWELLINGS MUST HAVE AT LEAST ONE EXTERIOR OUTLET AT THE FRONT AND THE BACK OF THE DWELLING. (CEC 210.52e)
5. RECEPTACLES MUST BE INSTALLED AT 12' O.C. MAXIMUM IN WALLS. WALLS LONGER THAN 2 FEET AND HALLS LONGER THAN 10' MUST HAVE A RECEPTACLE. A RECEPTACLE MUST BE PROVIDED WITHIN 3' OF BATHROOM SINKS. (CEC 210.52)
6. BOND ALL METAL GAS AND WATER PIPES TO GROUND. ALL GROUND CLAMPS MUST BE ACCESSIBLE AND OF AN APPROVED TYPE. (CEC 250.104)
7. FURNACES INSTALLED IN ATTICS AND CRAWL SPACES MUST HAVE AN ACCESS PLATFORM (CATWALK IN ATTICS, SLAB-ON-GRADE IN CRAWLSPACE), LIGHT, LIGHT SWITCH, AND RECEPTACLE IN THE SPACE. (CMC 904.10)
8. DWELLING TO HAVE A 120V POWERED SMOKE ALARM IN EVERY SLEEPING ROOM, OUTSIDE EACH SLEEPING ROOM, ON EVERY STORY OF THE DWELLING, INCLUDING BASEMENTS AND HABITABLE ATTICS, BUT NOT INCLUDING CRAWL SPACES OR UNINHABITABLE ATTICS. (R314.3)
9. SMOKE ALARM DEVICES SHALL BE INTERCONNECTED. (R314.4 & R315.7)
10. CARBON MONOXIDE ALARMS SHALL BE INSTALLED IN SLEEPING ROOMS WITHIN WHICH FUEL-BURNING APPLIANCES ARE INSTALLED, OUTSIDE OF EACH SLEEPING AREA, AND ON EACH OCCUPABLE LEVEL. CARBON MONOXIDE ALARMS ARE NOT REQUIRED IN DWELLINGS WHERE THERE IS NO FUEL-FIRED APPLIANCE OR ATTACHED GARAGE. (R315.1; R315.2)
11. ALL 120-VOLT 15 AND 20 AMP BRANCH CIRCUITS IN DWELLING UNITS EXCEPT THOSE IN BATHROOMS, UNFINISHED BASEMENTS, GARAGES AND OUTDOORS SHALL HAVE AFCI PROTECTION. (CEC 210.12)
12. RECEPTACLES ON 120-VOLT 15 AND 20 AMP CIRCUITS SHALL BE TAMPER RESISTANT. EXCEPT WHEN LOCATED MORE THAN 5.5' ABOVE THE FLOOR OR WHEN PART OF A LUMINAIRE OR APPLIANCE. (CEC 406.12)
13. VENT CLOTHES DRYER TO OUTSIDE OF BUILDING (NOT TO UNDERFLOOR AREA). VENT LENGTH SHALL BE 14' MAXIMUM AND THE VENT DIAMETER SHALL NOT BE LESS THAN 4". (CMC 504.4.2)
14. APPLIANCES AND RECEPTACLES INSTALLED IN GARAGES AND CARPORTS GENERATING A GLOW, SPARK, OR FLAME TO BE LOCATED 18" MIN. ABOVE THE FLOOR UNLESS LISTED AS FLAMMABLE VAPOR IGNITION RESISTANT. PROVIDE PROTECTIVE BOLLARD OR OTHER IMPACT BARRIER OR LOCATED OUT OF THE NORMAL PATH FOR VEHICLES. (CMC 305.1)

## STUDIO DESIGN

### SEALS

### PROJECT INFORMATION

**SMITH ADU**  
**1234 MAIN STREET**  
**ANYTOWN, CA**  
**100-100-100**

| DATE | DESCRIPTION |
|------|-------------|
|------|-------------|

### ISSUE INFORMATION

### DRAWING INFORMATION

|                 |                   |
|-----------------|-------------------|
| PROJECT NUMBER: | 2602              |
| SHEET SET:      |                   |
| FILENAME:       | AE-103            |
| SAVED DATE:     | 5/21/2026 1:53 PM |
| PLOT DATE:      | 5/21/2026 2:56 PM |
| LOGINNAME:      | S00740304         |
| DRAWN BY:       |                   |
| CHECKED BY:     |                   |


### SHEET TITLE

## ELECTRICAL AND LIGHTING PLAN

# AE-103


SHEET OF SHEETS



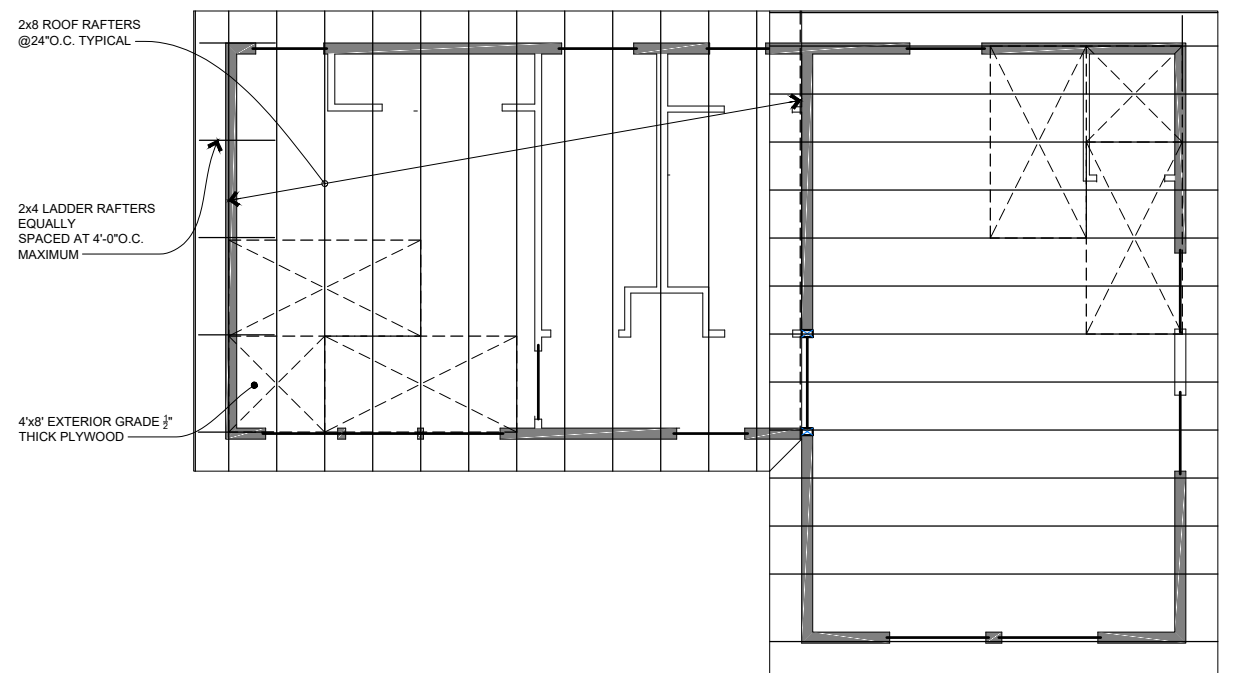

## ROOF/CEILING FRAMING PLAN

SCALE: 1/4" = 1'-0"

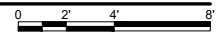

## STUDIO DESIGN

## SEALS

## PROJECT INFORMATION

**SMITH ADU  
1234 MAIN STREET  
ANYTOWN, CA  
100-100-100**

[illegible]

## ISSUE INFORMATION


### DRAWING INFORMATION

|                 |                   |
|-----------------|-------------------|
| PROJECT NUMBER: | 2602              |
| SHEET SET:      |                   |
| FILENAME:       | AS-104            |
| SAVED DATE:     | 5/21/2026 1:48 PM |
| PLOT DATE:      | 5/21/2026 2:55 PM |
| LOGINNAME:      | S00740304         |
| DRAWN BY:       |                   |
| CHECKED BY:     |                   |

**SHEET TITLE**


## ROOF FRAMING PLAN

# AS-104

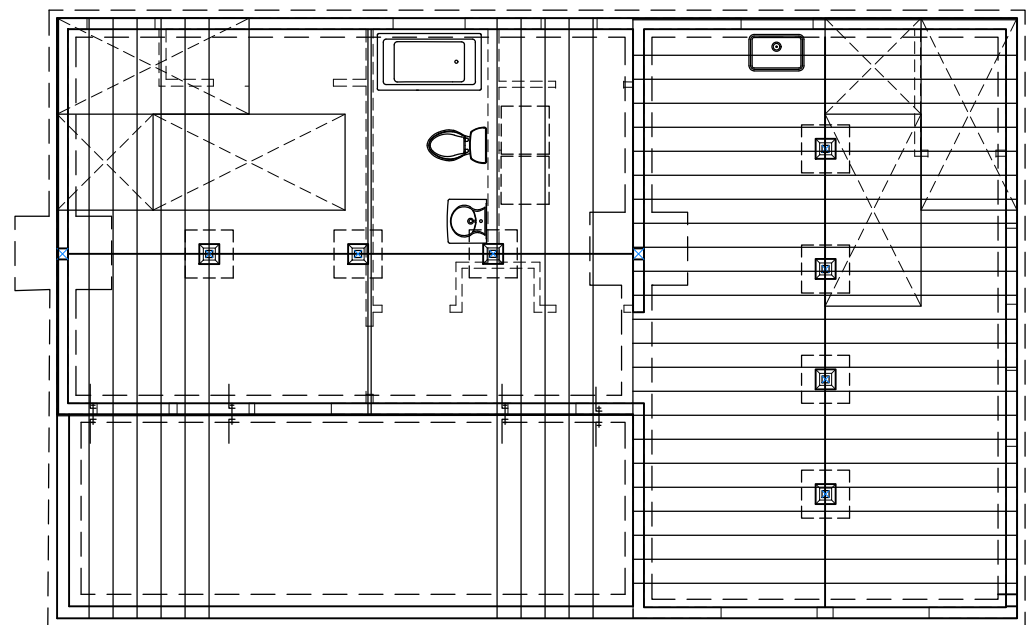

## FLOOR FRAMING AND FOUNDATION PLAN

SCALE: 1/4" = 1'-0"

 

## STUDIO DESIGN

## SEALS

## PROJECT INFORMATION

**SMITH ADU**  
**1234 MAIN STREET**  
**ANYTOWN, CA**  
**100-100-100**

[illegible]

## ISSUE INFORMATION

### DRAWING INFORMATION

|                 |                    |
|-----------------|--------------------|
| PROJECT NUMBER: | 2602               |
| SHEET SET:      |                    |
| FILENAME:       | AS-101             |
| SAVED DATE:     | 5/20/2026 11:48 AM |
| PLOT DATE:      | 5/21/2026 2:55 PM  |
| LOGINNAME:      | S00740304          |
| DRAWN BY:       |                    |
| CHECKED BY:     |                    |

## SHEET TITLE

# FLOOR FRAMING AND FOUNDATION PLAN

# AS-101